ТЕХНИЧЕСКОЕ ОПИСАНИЕ

здание

вид объекта недвижимого имущества

Здание

наименование объекта капитального строительства

Адрес (местоположение) объекта капитального строительства:

Субъект Российской Федерации	Российская Федерация, город Москва,	
Район	-	
Муниципальное образование	Тип	-
	Наименование	-
Населенный пункт	Тип	-
	Наименование	-
Улица (проспект, переулок и т.д.)	Тип	улица
	Наименование	Рабочая
Номер дома	91	
Номер корпуса	-	
Номер строения	4	
Литера	-	
Иное описание местоположения	вн. тер. г. муниципальный округ Таганский	

Сведения о ранее произведенной постановке на государственный учет ОКС

Кадастровый номер здания	*77:01:006043:1019*
Кадастровый номер помещения	-

Сведения о кадастровом инженере:
Фамилия, имя, отчество (при наличии отчества) Жукова Вера Алексеевна
№ квалификационного аттестата кадастрового инженера *50-10-234*
Контактный телефон: ***8-925-642-58-92***
Почтовый адрес и адрес электронной почты, по которым осуществляется связь с кадастровым инженером: Московская область, Одинцовский район, г. Одинцово, улица Говорова, дом 18/1, офис 403; o-geo@mail. ru

Техническое описание составлено по состоянию на *15 февраля 2024* г.

Сокращенное наименование юридического лица, если кадастровый инженер является работником юридического лица: ООО «Октант»	
Кадастровый инженер	Подпись, печать
Жукова В. А.	

2. Опись (состав) технического описания

№ п/п	Наименование раздела, прилагаемых документов:	№ стр.
1	Титульный лист	1
2	Опись (состав) технического описания	2
3	Общие сведения	3
4	Состав объекта	4
5	Ситуационный план	5
6	План этажа	6-8
7	Экспликация к поэтажному плану	9-14
8	Сведения о правообладателях объекта	15

3. Общие сведения

1	Вид объекта	Здание
2	Назначение	нежилое
3	Наименование объекта	здание
4	Год завершения строительства	1966
5	Площадь застройки, кв.м.	3264,1
6	Общая площадь здания, кв.м. *	8964,1
7	Площадь по сумме помещений, кв.м.	8555,5
8	Этажность (в том числе подземная).	3 (0)
9	Примечание	Наименование, местоположение, назначение помещений, год постройки и материал стен объекта указаны заказчиком кадастровых работ.

* *Площадь нежилого здания, определенная с учетом Требований к определению площади здания, сооружения и помещения, утвержденных приказом Росреестра от 23 октября 2020 г. N П/0393 (является основной характеристикой объекта недвижимости при государственном кадастровом учете и регистрации права), составила 8964,1 кв.м.*

Документы, представленные для производства технического описания:	- Выписка из ЕГРН от 08.02.2024 г., № КУВИ-001/2024-39950282

4. Состав объекта

№ на плане (литера)	Наименование зданий, сооружений	Материал стен	Параметр			Площадь застройки кв.м	Высота, м	Объем, куб.м
			наименование параметра	единица измерения	всего			
1	2	3	4	5	6	7	8	9
-	Здание	крупнопанельные	общая площадь	кв. м	8555,5	3264,1	ср. 14,71	45647

5. Ситуационный план

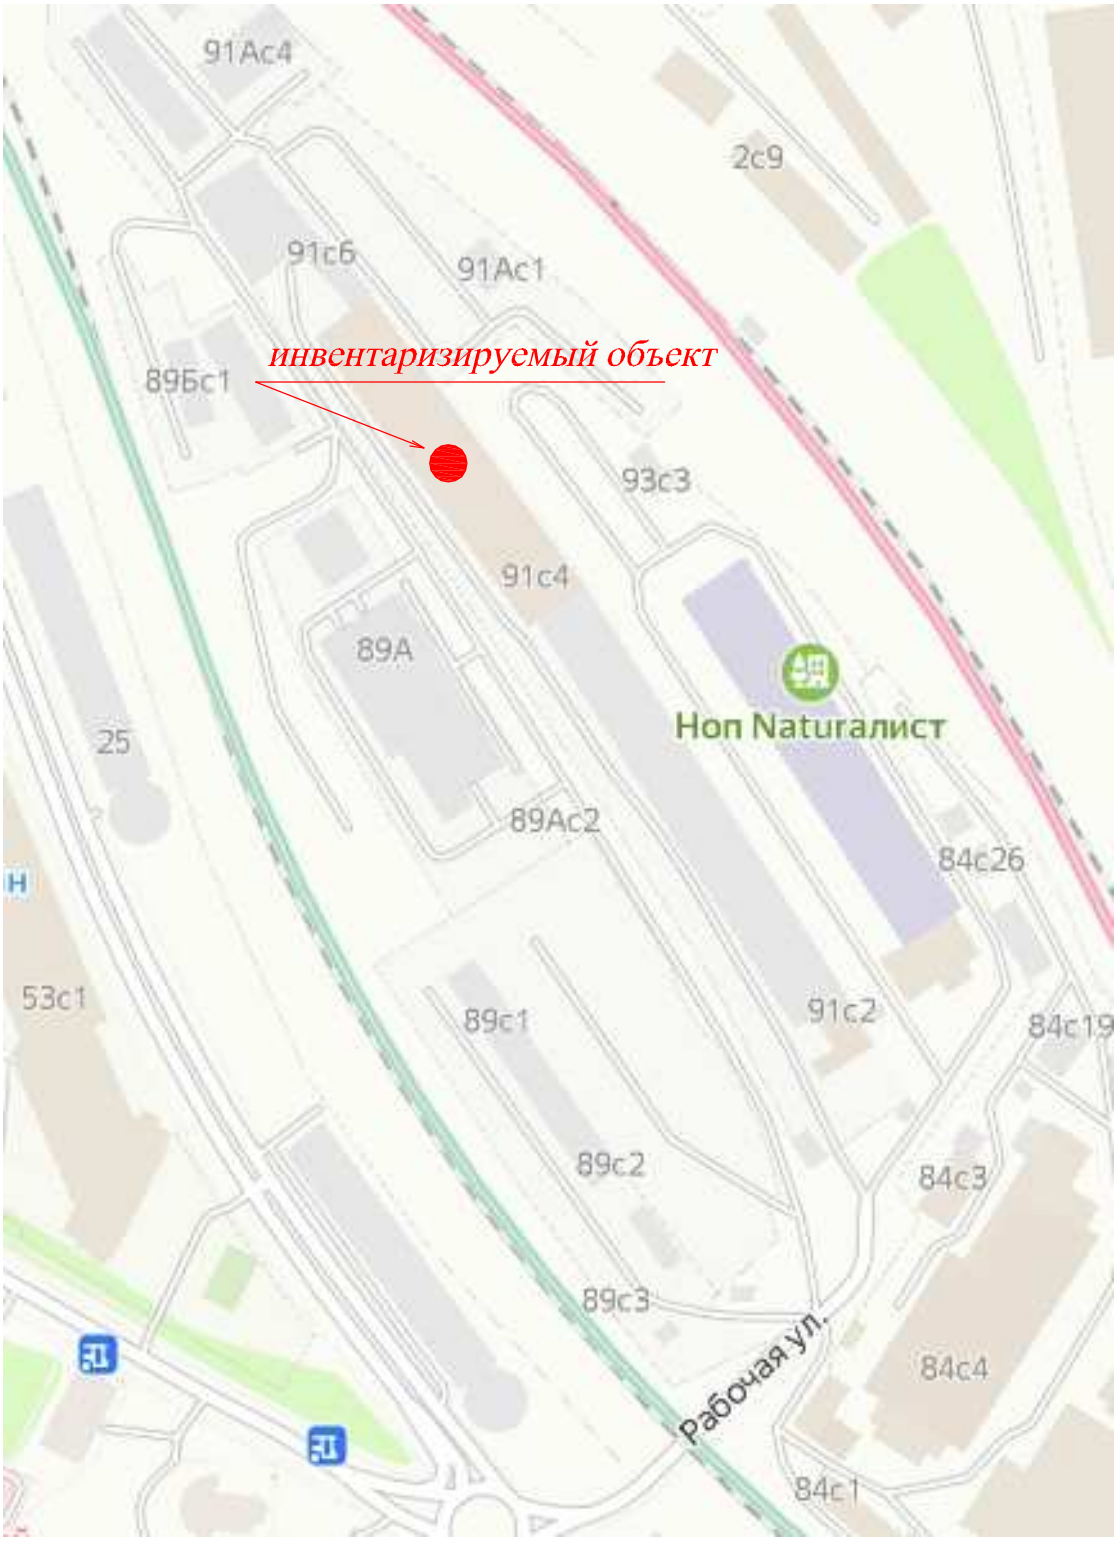

6. План этажа

1 этаж

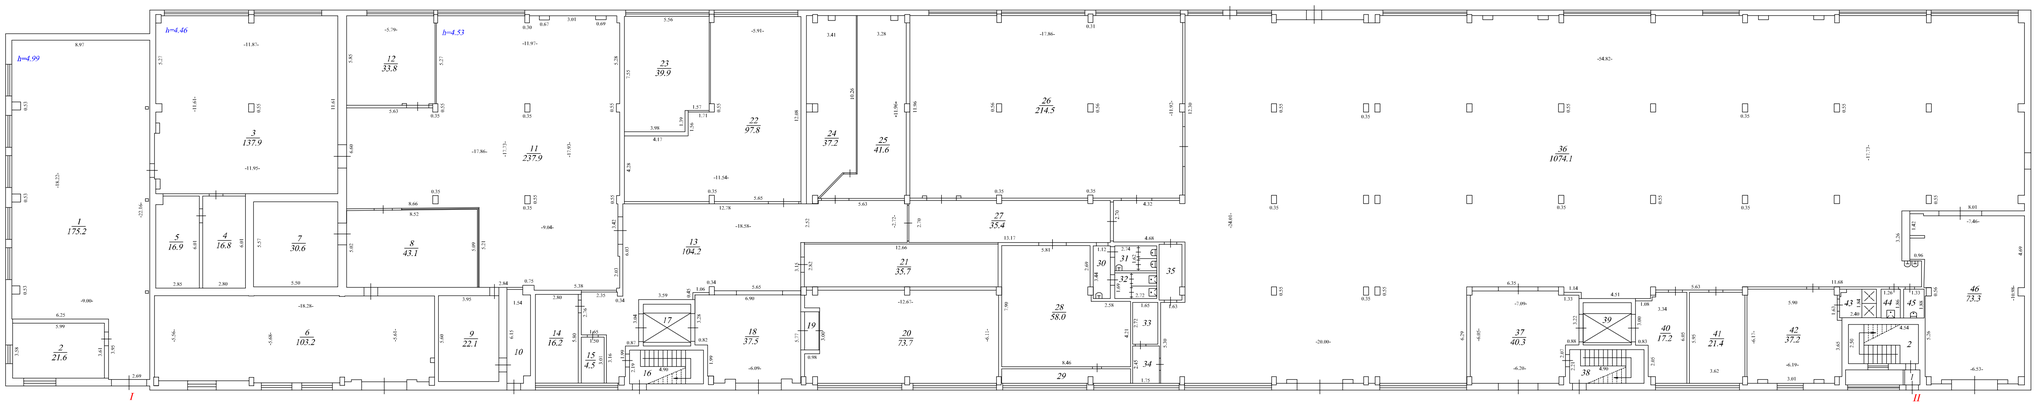

Масштаб 1:200

6. План этажа

2 этаж

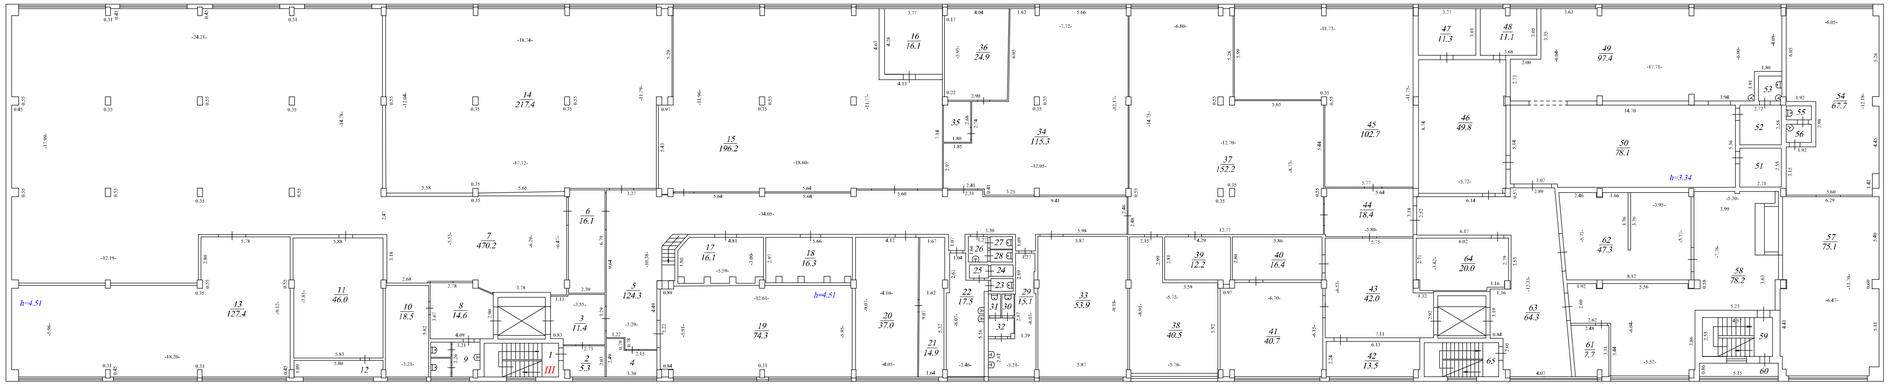

Масштаб 1:200

6. План этажа

3 этаж

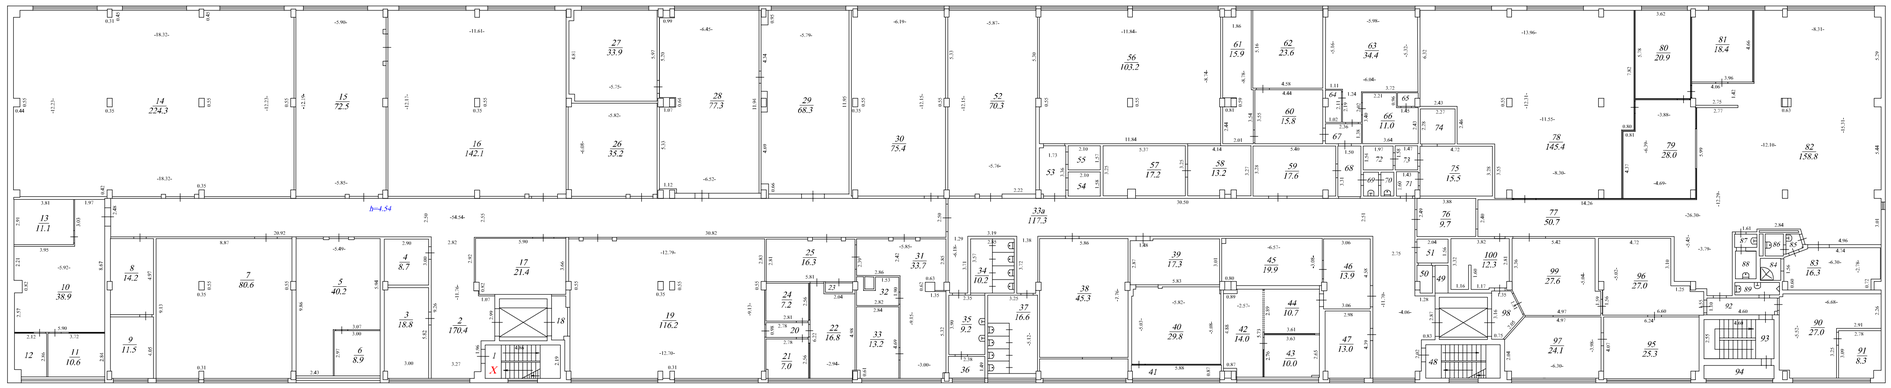

Масштаб 1:200

7. Экспликация к плану этажа здания (строения)

этаж	№ помещения	№ по плану	Назначение помещений	Площадь помещений	Высота
1	I	1	котельная	175,2	h=4,99
		2	служебное	21,6	
		3	помещение	137,9	h=4,99
		4	подсобное	16,8	
		5	подсобное	16,9	
		6	склад	103,2	
		7	склад	30,6	
		8	помещение	43,1	
		9	электрощитовая	22,1	
		10	подсобное	9,0	
		11	помещение	237,9	h=4,53
		12	помещение	33,8	
		13	коридор	104,2	
		14	подсобное	16,2	
		15	подсобное	4,5	
		16	лестничная клетка	10,8	
		17	лифт	6,0	
		18	коридор	37,5	
		19	коридор	2,3	
		20	помещение	73,7	
		21	помещение	35,7	
		22	помещение	97,8	
		23	помещение	39,9	
		24	помещение	37,2	
		25	помещение	41,6	
		26	помещение	214,5	
		27	коридор	35,4	
		28	венткамера	58,0	
		29	венткамера	7,2	
		30	санузел	3,9	
		31	санузел	4,4	
		32	санузел	4,6	
		33	подсобное	4,5	
		34	подсобное	4,3	
		35	подсобное	5,1	
		36	помещение	1074,1	
		37	коридор	40,3	
		38	лестничная клетка	10,8	

		39	лифт	6,0	
		40	мастерская	17,2	
		41	мастерская	21,4	
		42	раздевалка	37,2	
		43	душевая	4,3	
		44	санузел	2,3	
		45	санузел	2,5	
		46	тех. помещение	73,3	
Итого по помещению I:				***2986,8***	
1	II	1	тамбур	1,0	
		2	лестничная клетка	11,4	
Итого по помещению II:				***12,3***	
2	III	1	лестничная клетка	10,7	
		2	коридор	5,3	
		3	коридор	11,4	
		4	подсобное	6,5	
		5	коридор	124,3	
		6	коридор	16,1	
		7	помещение	470,2	
		8	коридор	14,6	
		9	санузел	7,0	
		10	кабинет	18,5	
		11	тех. помещение	46,0	
		12	тех. помещение	6,3	
		13	помещение	127,4	h=4,51
		14	помещение	217,4	
		15	помещение	196,2	
		16	подсобное	16,1	
		17	подсобное	16,1	
		18	подсобное	16,3	
		19	помещение	74,3	h=4,53
		20	помещение	37,0	
		21	помещение	14,9	
		22	подсобное	17,5	
		23	санузел	1,2	
		24	санузел	1,2	
		25	санузел	1,0	
		26	санузел	2,1	
		27	санузел	1,2	
		28	санузел	1,2	
		29	подсобное	15,1	

		30	санузел	1,1	
		31	санузел	1,2	
		32	санузел	2,0	
		33	помещение	53,9	
		34	помещение	115,3	
		35	подсобное	4,7	
		36	помещение	24,9	
		37	помещение	152,2	
		38	помещение	40,5	
		39	подсобное	12,2	
		40	помещение	16,4	
		41	помещение	40,7	
		42	помещение	13,5	
		43	помещение	42,0	
		44	коридор	18,4	
		45	помещение	102,7	
		46	кабинет	49,8	
		47	кабинет	11,3	
		48	кабинет	11,1	
		49	помещение	97,4	
		50	помещение	78,1	
		51	подсобное	6,9	
		52	подсобное	7,0	
		53	санузел	2,5	
		54	помещение	67,7	
		55	санузел	1,5	
		56	санузел	2,0	
		57	помещение	75,1	
		58	помещение	78,2	
		59	лестничная клетка	11,7	
		60	подсобное	4,4	
		61	подсобное	7,7	
		62	помещение	47,3	
		63	коридор	64,3	
		64	тех. помещение	20,0	
		65	лестничная клетка	10,7	
Итого по помещению III:				***2789,5***	
3	X	1	лестничная клетка	10,6	
		2	коридор	170,4	h=4,54
		3	кабинет	18,8	
		4	подсобное	8,7	
		5	помещение	40,2	
		6	подсобное	8,9	

		7	помещение	80,6	
		8	кабинет	14,2	
		9	кабинет	11,5	
		10	помещение	38,9	
		11	подсобное	10,6	
		12	подсобное	5,9	
		13	кабинет	11,1	
		14	помещение	224,3	
		15	помещение	72,5	
		16	помещение	142,1	
		17	помещение	21,4	
		18	тамбур	2,9	
		19	помещение	116,2	
		20	коридор	2,7	
		21	подсобное	7,0	
		22	помещение	16,8	
		23	шкаф	1,0	
		24	подсобное	7,2	
		25	помещение	16,3	
		26	тех. помещение	35,2	
		27	кабинет	33,9	
		28	помещение	77,3	
		29	помещение	68,3	
		30	помещение	75,4	
		31	помещение	33,7	
		32	подсобное	4,6	
		33	помещение	13,2	
		33а	коридор	117,3	
		34	санузел	10,2	
		35	санузел	9,2	
		36	подсобное	3,5	
		37	санузел	16,6	
		38	помещение	45,3	
		39	помещение	17,3	
		40	помещение	29,8	
		41	подсобное	5,1	
		42	помещение	14,0	
		43	помещение	10,0	
		44	коридор	10,7	
		45	помещение	19,9	
		46	помещение	13,9	
		47	помещение	13,0	
		48	лестничная клетка	10,6	
		49	подсобное	1,5	

		50	подсобное	1,7	
		51	подсобное	3,2	
		52	помещение	70,3	
		53	коридор	5,6	
		54	подсобное	3,3	
		55	подсобное	3,3	
		56	помещение	103,2	
		57	кабинет	17,2	
		58	помещение	13,2	
		59	помещение	17,6	
		60	помещение	15,8	
		61	подсобное	15,9	
		62	помещение	23,6	
		63	помещение	34,4	
		64	подсобное	2,0	
		65	подсобное	1,1	
		66	подсобное	11,0	
		67	коридор	3,3	
		68	коридор	5,0	
		69	санузел	1,5	
		70	санузел	1,3	
		71	коридор	2,2	
		72	подсобное	3,0	
		73	подсобное	2,3	
		74	подсобное	5,2	
		75	помещение	15,5	
		76	коридор	9,7	
		77	помещение	50,7	
		78	помещение	145,4	
		79	помещение	28,0	
		80	кабинет	20,9	
		81	кабинет	18,4	
		82	помещение	158,8	
		83	помещение	16,3	
		84	душевая	1,9	
		85	санузел	1,1	
		86	санузел	1,7	
		87	санузел	1,2	
		88	санузел	2,4	
		89	санузел	2,4	
		90	кабинет	27,0	
		91	кабинет	8,3	
		92	коридор	5,1	
		93	подсобное	11,7	

		94	подсобное	2,7	
		95	помещение	25,3	
		96	помещение	27,0	
		97	помещение	24,1	
		98	тамбур	4,9	
		99	помещение	27,6	
		100	раздевалка	12,3	
Итого по помещению Х:				***2766,9***	
Всего по сумме помещений:				***8555,5***	

8. Сведения о правообладателях объекта

Субъект права: для физических лиц - фамилия, имя, отчество; для юридических лиц - наименование в соответствие с уставом	Вид права	Сведения о регистрации права
1	2	3
Акционерное общество «ДИАПАЗОН»	Собственность	**77-01/01-013/2000-1335в от 12.07.2000**

Техническое описание

Выполнил	
Ф.И.О. Кадастрового инженера	Подпись
Жукова В. А.	